


Floor Slab

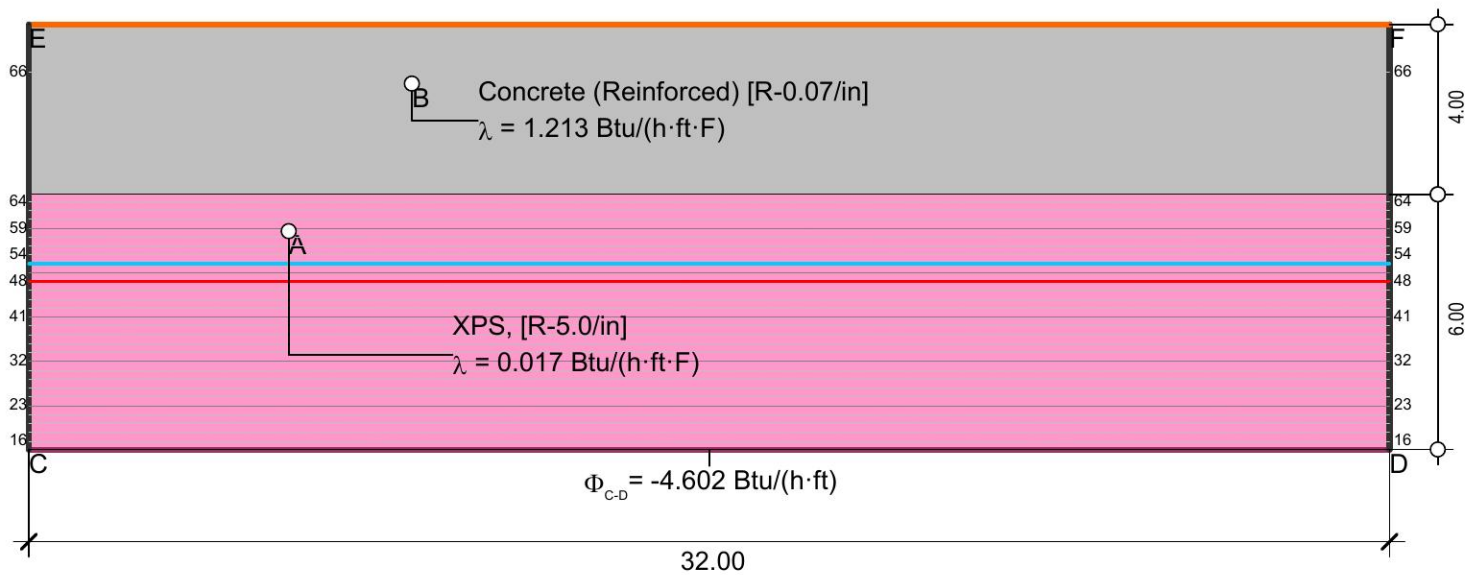

$$U_{eq \text{ C-D}} = \frac{4.602}{54.0 \cdot 2.667} = 0.0320 \text{ Btu}/(\text{h}\cdot\text{ft}^2\cdot\text{F}) = R-31.3$$

Boundary Condition	q[Btu/(h·ft ²)]	θ[F]	h[Btu/(h·ft ² ·F)]	ε
Ext. No Rse		14.000	17.611	
Interior, heat flux, downwards		68.000	1.036	
Symmetry/Model section	0.000			

Material	λ[Btu/(h·ft·F)]	ε
Concrete (Reinforced) [R-0.07/in]	1.213	0.900
XPS, [R-5.0/in]	0.017	0.900