


Wall BG

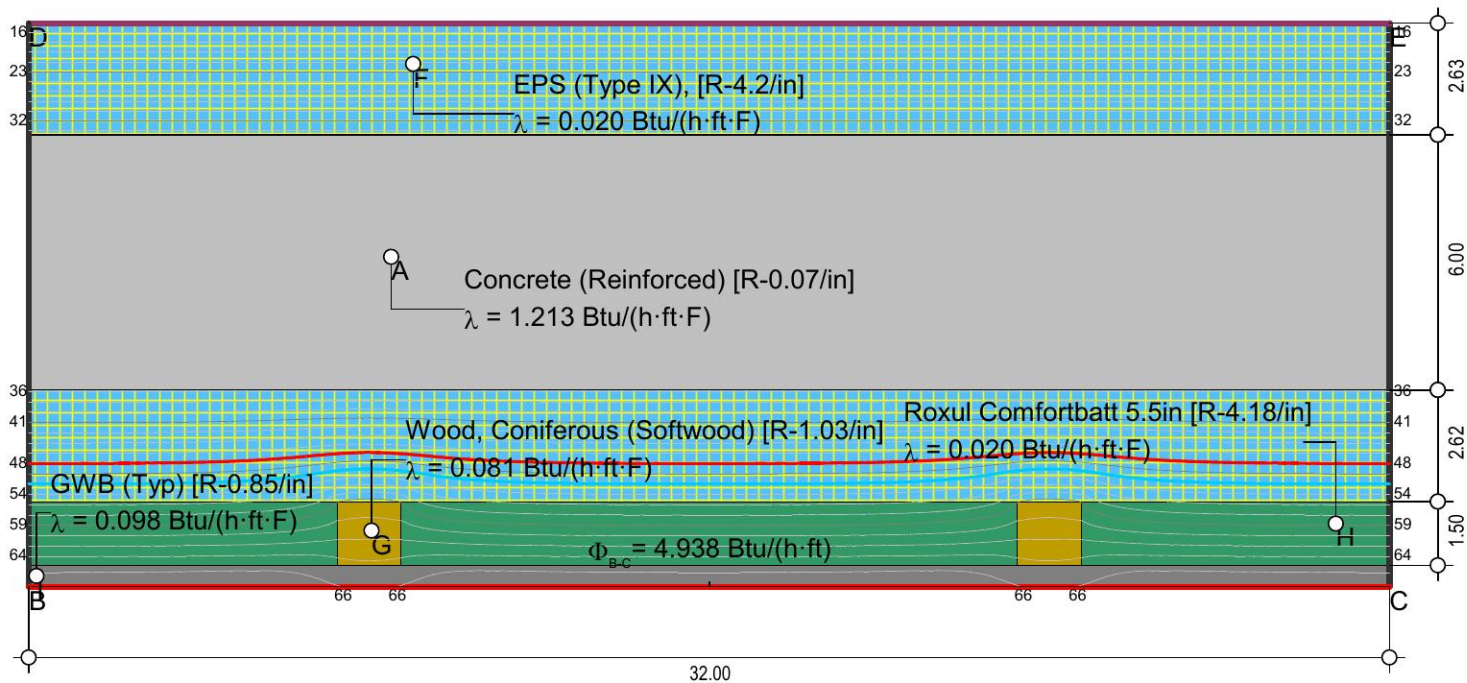

U_{eq B-C} = $\frac{4.938}{54.0 \cdot 2.667} = 0.0343 \text{ Btu}/(\text{h}\cdot\text{ft}^2\cdot\text{F})$ = R-29.2

Boundary Condition	q[Btu/(h·ft ²)]	θ[°F]	h[Btu/(h·ft ² ·F)]	ε	Material	λ[Btu/(h·ft·F)]	ε
Ext. No Rse		14.000	17.611		Concrete (Reinforced) [R-0.07/in]	1.213	0.900
Interior, normal, horizontal		68.000	1.355		EPS (Type IX), [R-4.2/in]	0.020	0.900
Symmetry/Model section	0.000				GWB (Typ) [R-0.85/in]	0.098	0.900
					Roxul Comfortbatt 5.5in [R-4.18/in]	0.020	0.900
					Wood, Coniferous (Softwood) [R-1.03/in]	0.081	0.900